
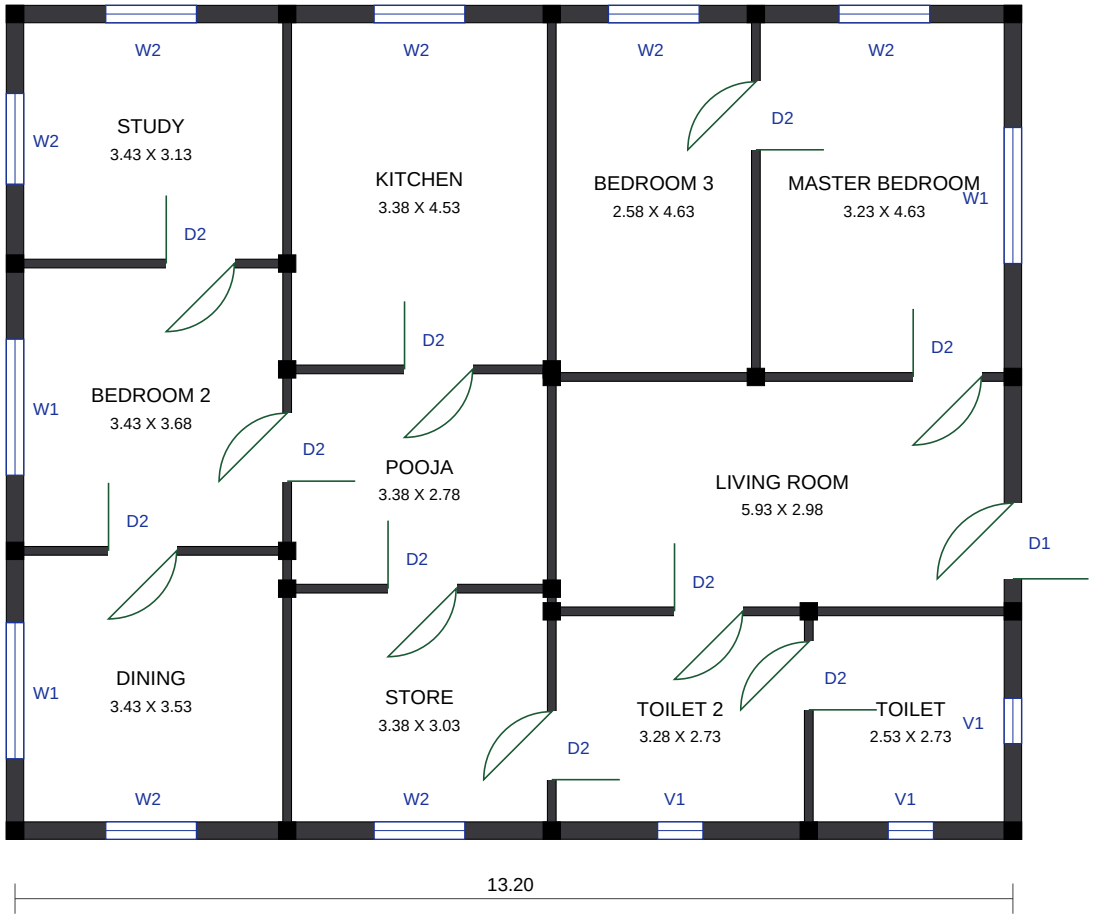


DOOR & WINDOW SCHEDULE

D1 1000 X 2100 FLUSH DOOR 2 NOS
D2 900 X 2100 FLUSH DOOR 19 NOS
W1 1800 X 1200 ALUMINIUM SLIDING WINDOW 7 NOS
W2 1200 X 1200 ALUMINIUM SLIDING WINDOW 12 NOS
V1 600 X 600 VENTILATOR 6 NOS

GROUND FLOOR PLAN

SCALE 1:100 ALL LEVELS AS PER SECTION A-A
ALL DIMENSIONS IN METRES

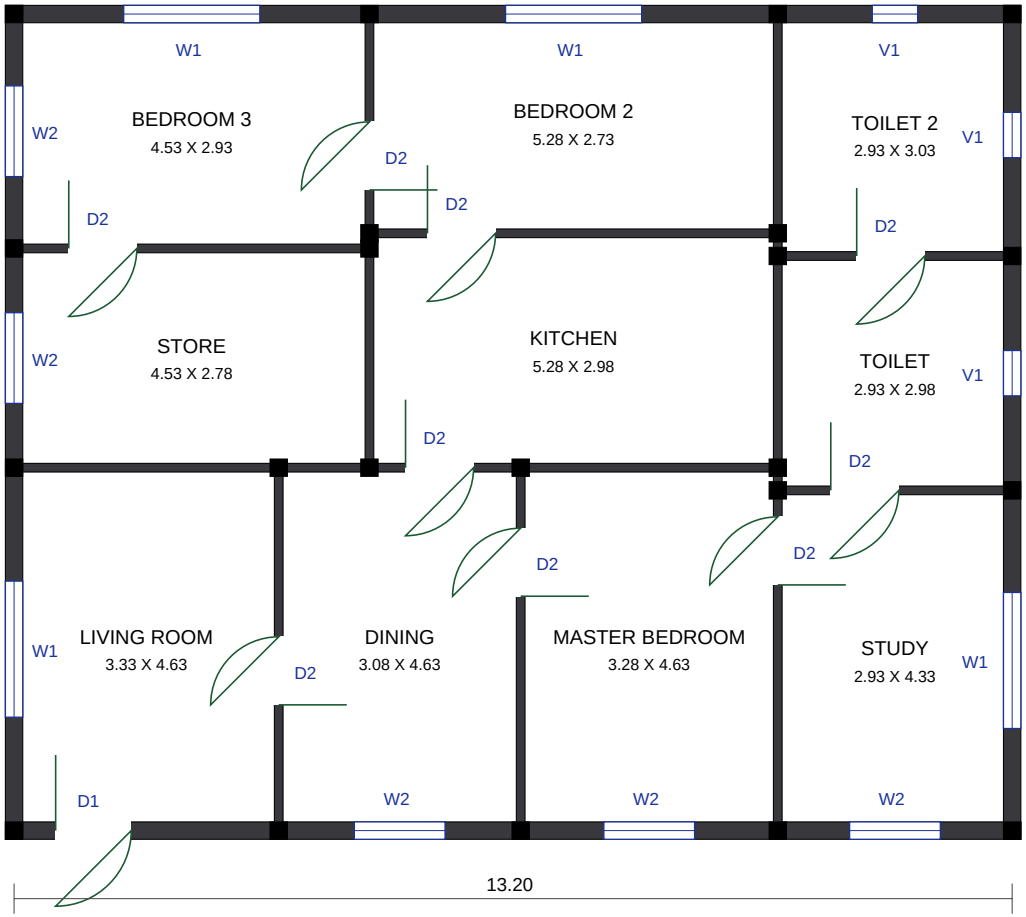

FIRST FLOOR PLAN


SCALE 1:100 ALL LEVELS AS PER SECTION A-A

ALL DIMENSIONS IN METRES

SILL LVL +1.350


LINTEL LVL +2.550

ROOF SLAB 125 THK

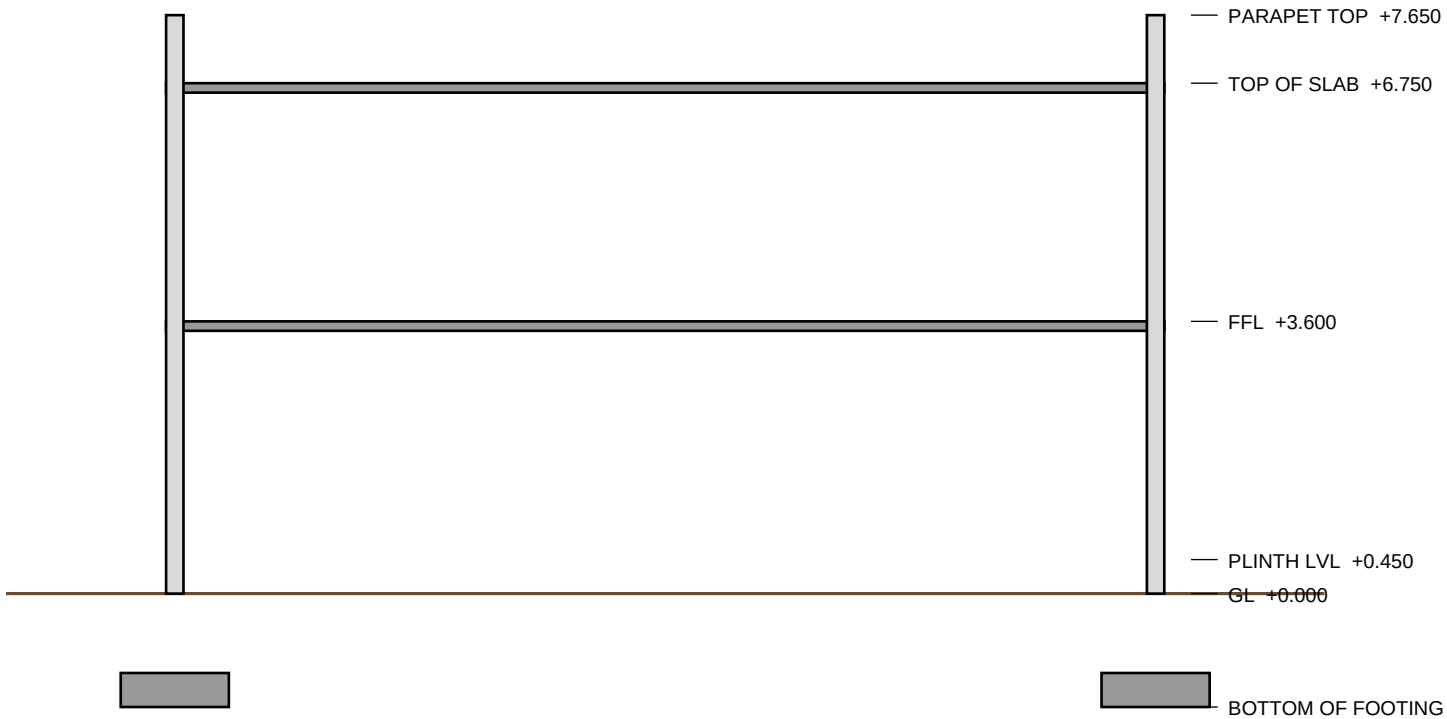

SECTION A-A

SCALE 1:100 LEVELS IN METRES

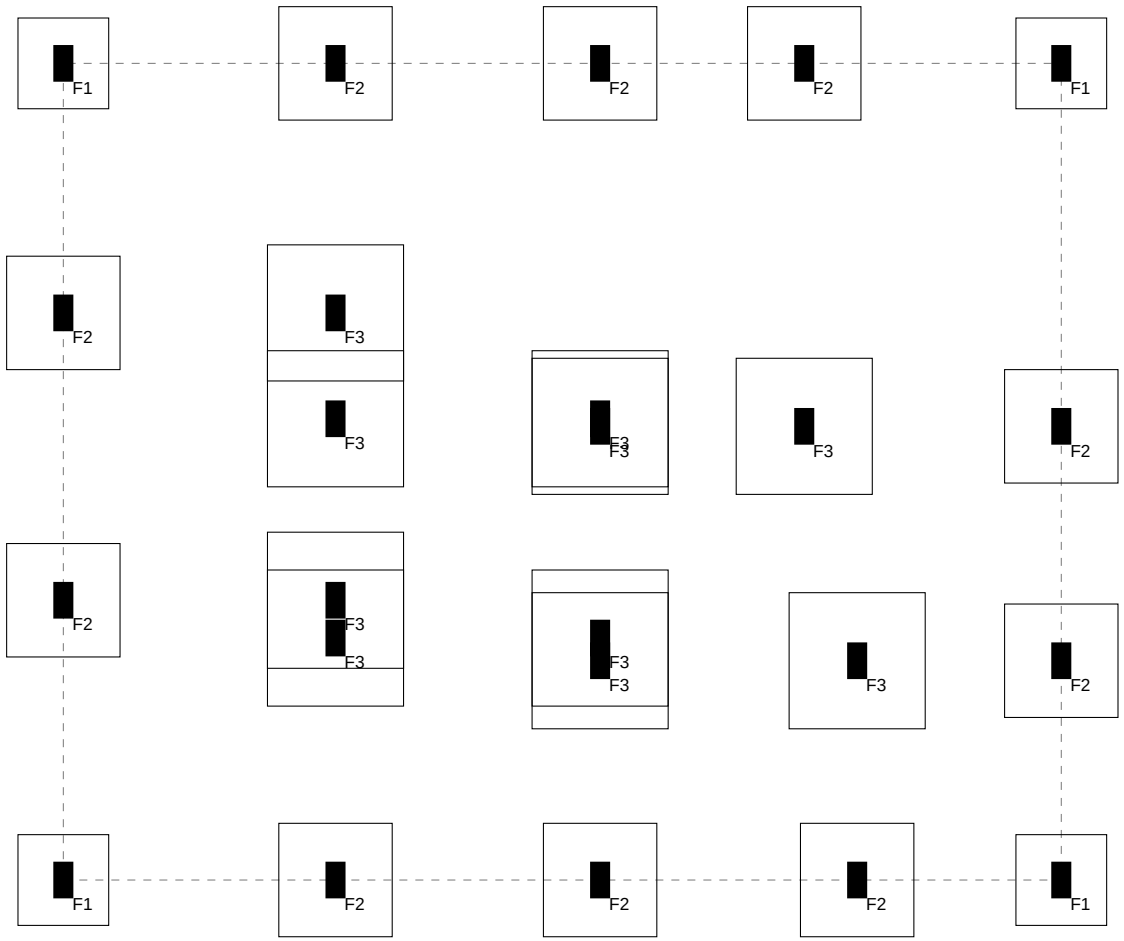

FOOTING SCHEDULE

F1	1200 X 1200 X 400	Y10 @ 150 BOTH WAYS	4 NOS
F2	1500 X 1500 X 450	Y12 @ 150 BOTH WAYS	10 NOS
F3	1800 X 1800 X 500	Y12 @ 125 BOTH WAYS	10 NOS

PCC 1:4:8 100 THK BELOW ALL FOOTINGS

BOTTOM OF FOOTING -1.500

FOUNDATION PLAN

SCALE 1:100 STRUCTURAL

COLUMN SCHEDULE

C1 230 X 450 4-Y16 + 2-Y12 TIES Y8 @ 150 24 NOS

BEAM SCHEDULE

PB1 230 X 300 TOP 2-Y12 BOT 2-Y12 STR Y8 @ 150 L= 103.70 M PLINTH BEAMS

B1 230 X 450 TOP 2-Y12 BOT 3-Y16 STR Y8 @ 150 L= 103.70 M FIRST FLOOR BEAMS

RB1 230 X 450 TOP 2-Y12 BOT 3-Y12 STR Y8 @ 150 L= 100.80 M ROOF BEAMS

SLAB SCHEDULE

S1 SLAB 125 THK MAIN Y10 @ 150 DIST Y8 @ 200

COLUMN & BEAM SCHEDULE

STRUCTURAL CONCRETE M25 STEEL FE500D